
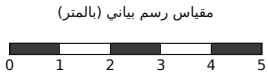


بيانات الأرض والإشغال	
أبعاد قطعة الأرض	م 20.00 × 20.00
مساحة قطعة الأرض	م ² 400.00
نسبة الإشغال المسموحة	60 %
أقصى مسطح بناء مسموح	م ² 240.00
أبعاد المبنى المنفذ	م 16.00 × 15.00
مسطح البناء بالدور	م ² 240.00
الارتداد الأمامي	م 3.00
الارتداد الخلفي	م 2.00
الارتداد الجانبي (يمين/يسار)	م 2.00
صافي المساحات المكشوفة	م ² 160.00
نسبة الإشغال المحققة	
240 ÷ 400 = 60.0 %	

ملاحظات الموقع

- المبنى دوران (أرضي + أول) بشقة لكل دور.
- المدخل الرئيسي أمامي من الشارع ويؤدي إلى بهو مشترك ومنه إلى السلم الخلفي.
- ممر جانبي مرصوف عرض 2.00 م يصل الواجهة الأمامية بالحديقة الخلفية ويخدم السلم.
- المنور المكشوف 3.10 × 3.00 م يخترق الدورين لإضاءة وتهوية الحمامات والممر.
- أسوار الأرض ارتفاع 2.20 م مبانٍ ودخلات معدنية.
- الارتدادات مطابقة لاشتراطات المنطقة، وتراجع مع الإدارة الهندسية قبل التنفيذ.

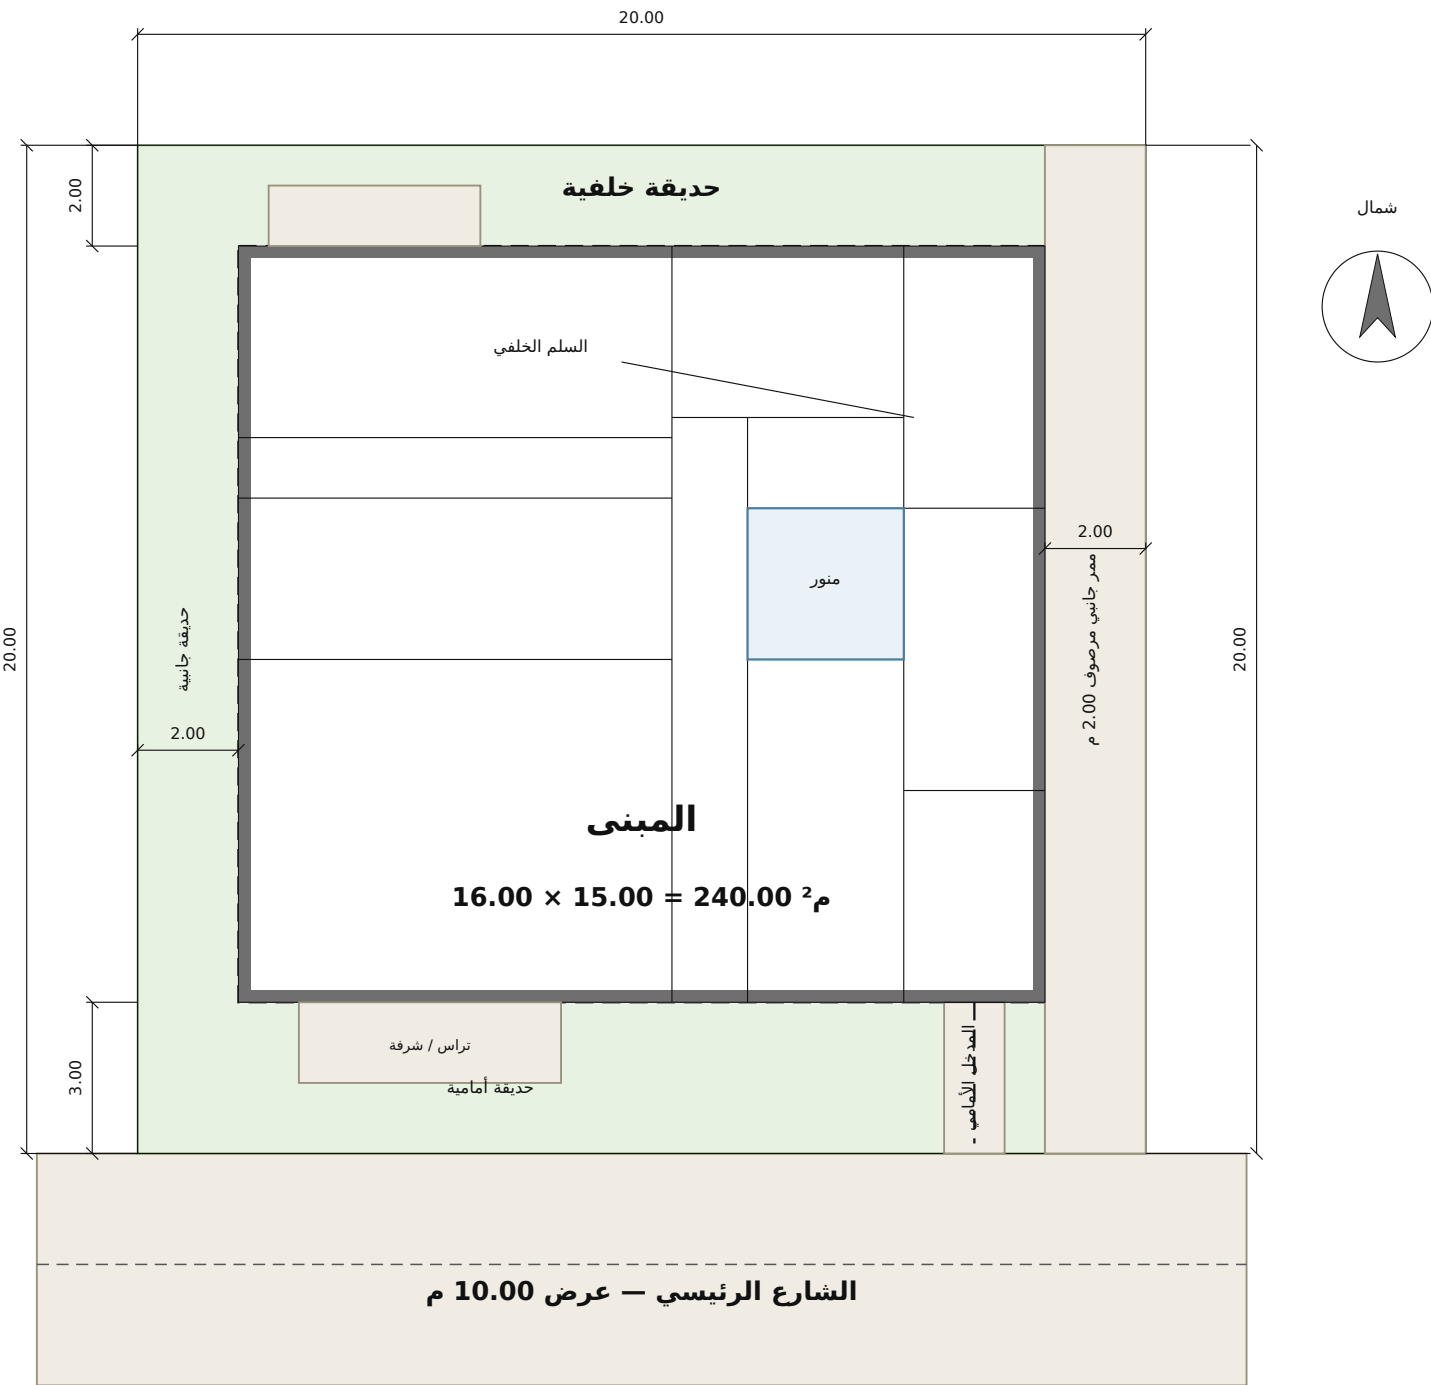

منزل سكني بشقتين - قطعة أرض 400 م ²		
الموقع العام والارتدادات		
مقياس 1:150	رسم ابتدائي (تصميمي)	لوحة 01

Ground Floor Plan — 1:100



جدول مساحات الشقة

المساحات المشتركة

ملاحظات

- جميع الغرف والصالة والمطبخ والحمامين لها إضاءة
- وتهوية طبيعية مباشرة (نسبة الفتحات $> 10\%$).
- سمك الحوائط الخارجية 25 سم والقواطع 12 سم.
- ارتفاع الدور 3.30 م والصافي 3.05 م.
- الأبعاد بالترتيب ومحسوبة على محاور الحوائط.



منزل سكني بشقتين - قطعة أرض 400 م²

مسقط الدور الأرضي


لوحة 02

رسم ابتدائی (تصمیمی)

مقیاس 1:100

مسقط الدور الأول

First Floor Plan — 1:100

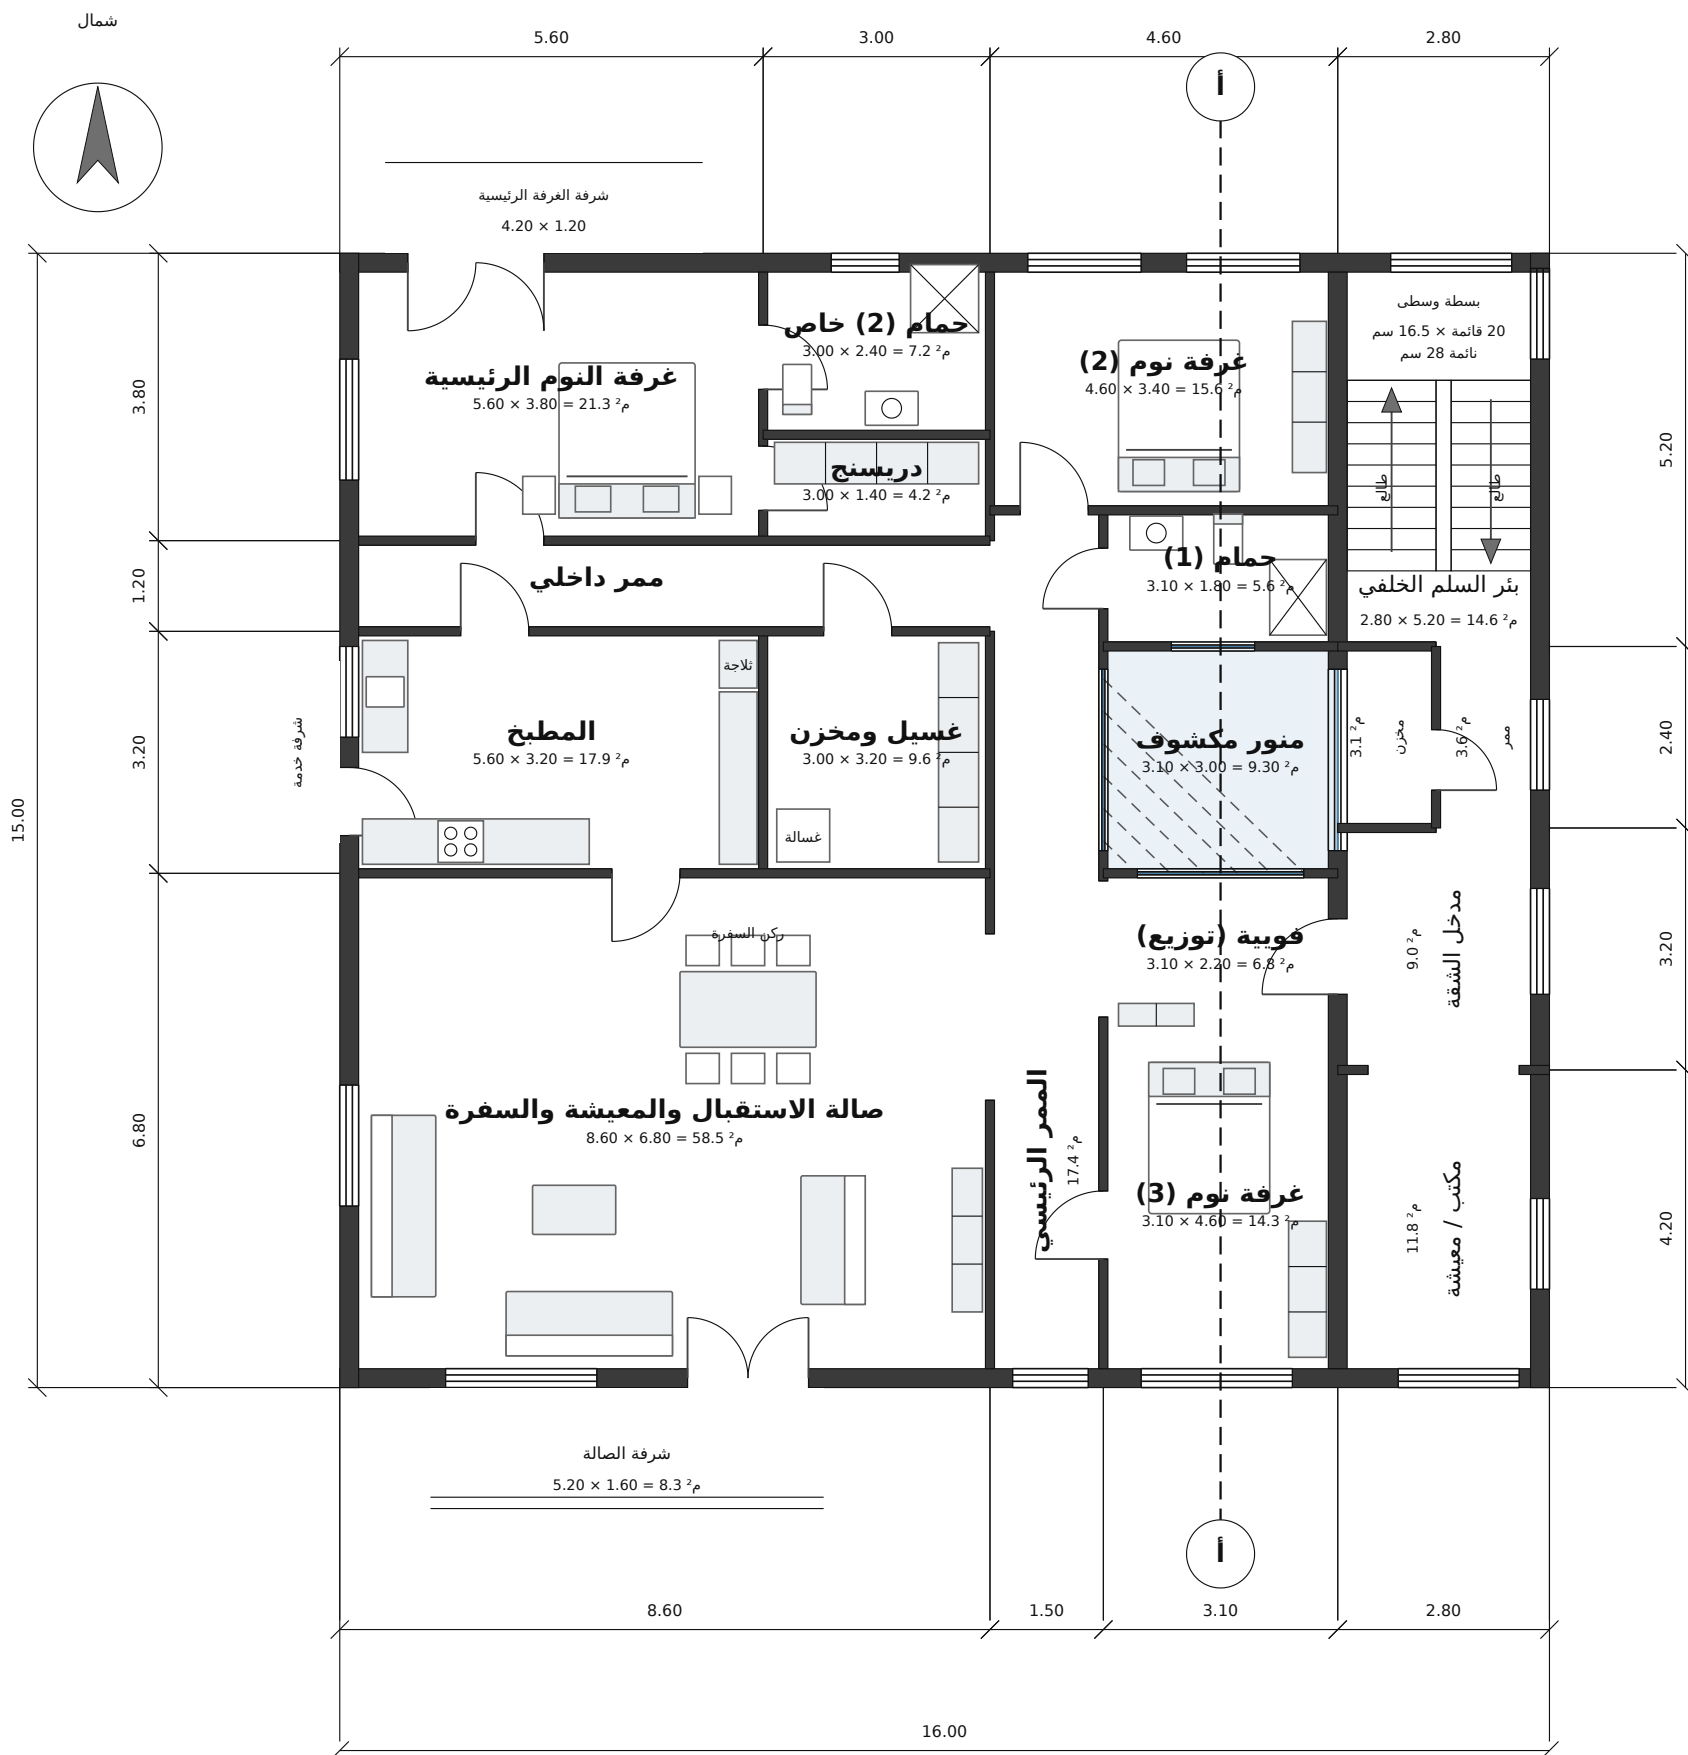

جدول مساحات الشقة

صالة استقبال ومعيشة وسفرة	58.5 م ²
غرفة النوم الرئيسية	21.3 م ²
غرفة نوم (2)	15.6 م ²
غرفة نوم (3)	14.3 م ²
المطبخ	17.9 م ²
حمام (1) مشترك	5.6 م ²
حمام (2) خاص	7.2 م ²
درستج	4.2 م ²
غرفة غسيل ومخزن	9.6 م ²
ممرات وفوية	34.5 م ²
منور مكشوف	9.3 م ²
مكتب / معيشة صغيرة	11.8 م ²
مدخل الشقة (فوية)	9.0 م ²
ممر ومخزن	6.7 م ²
صافي المسطح المسقوف (بدون المنور)	216.1 م ²
إجمالي مسطح الشقة	225.4 م ²

المساحات المشتركة

بنر السلم الخلفي	14.6 م ²
مسطح الدور الكلي	240.00 م ²

ملاحظات

- مسطح بهو المدخل والممر المشترك بالدور الأرضي
- يُضم لشقة الدور الأول لتعويض مساحته.
- جميع الغرف والصالة والمطبخ والحمامين لها إضاءة وتهوية طبيعية مباشرة (نسبة الفتحات > 10%).
- سمك الحوائط الخارجية 25 سم والقواطع 12 سم.
- ارتفاع الدور 3.30 م والصافي 3.05 م.
- الأبعاد بالمتر ومحسوبة على محاور الحوائط.

مقياس رسم بياني (بالمتر)

منزل سكني بشقتين - قطعة أرض 400 م²

مسقط الدور الأول

لوحة 03

رسم ابتدائي (تصميمي)

مقياس 1:100

قطاع رأسي أ-أ


Section A-A — 1:75

المناسيب والارتفاعات

منسوب أرضية الدور الأرضي	م 0.60 +
ارتفاع الدور (أرضية لأرضية)	م 3.30
الارتفاع الصافي للدور	م 3.05
سمك البلاطة الخرسانية	م 0.25
منسوب سطح المبنى	م 7.20 +
ارتفاع سور السطح	م 1.00
أعلى نقطة بالمبنى (غرفة السلم)	م 10.00 +

ملاحظات إنشائية

- الهيكل خرسانة مسلحة: قواعد منفصلة + سمات
- + أعمدة + كمرات + بلاطة مصمتة 25 سم.
- شبكة الأعمدة في حدود 4.00 - 5.00 م.
- المباني طوب أحمر/أسمنتي 25 سم للخارجي
- و 12 سم للقواطع الداخلية.
- عزل مائي للسطح وللحمامات والمنور.
- ميول السطح 1.5% نحو مصارف المطر.
- الارتفاع الكلي لا يتعدى 1.5 × عرض الشارع
- طبقاً لقانون البناء الموحد.

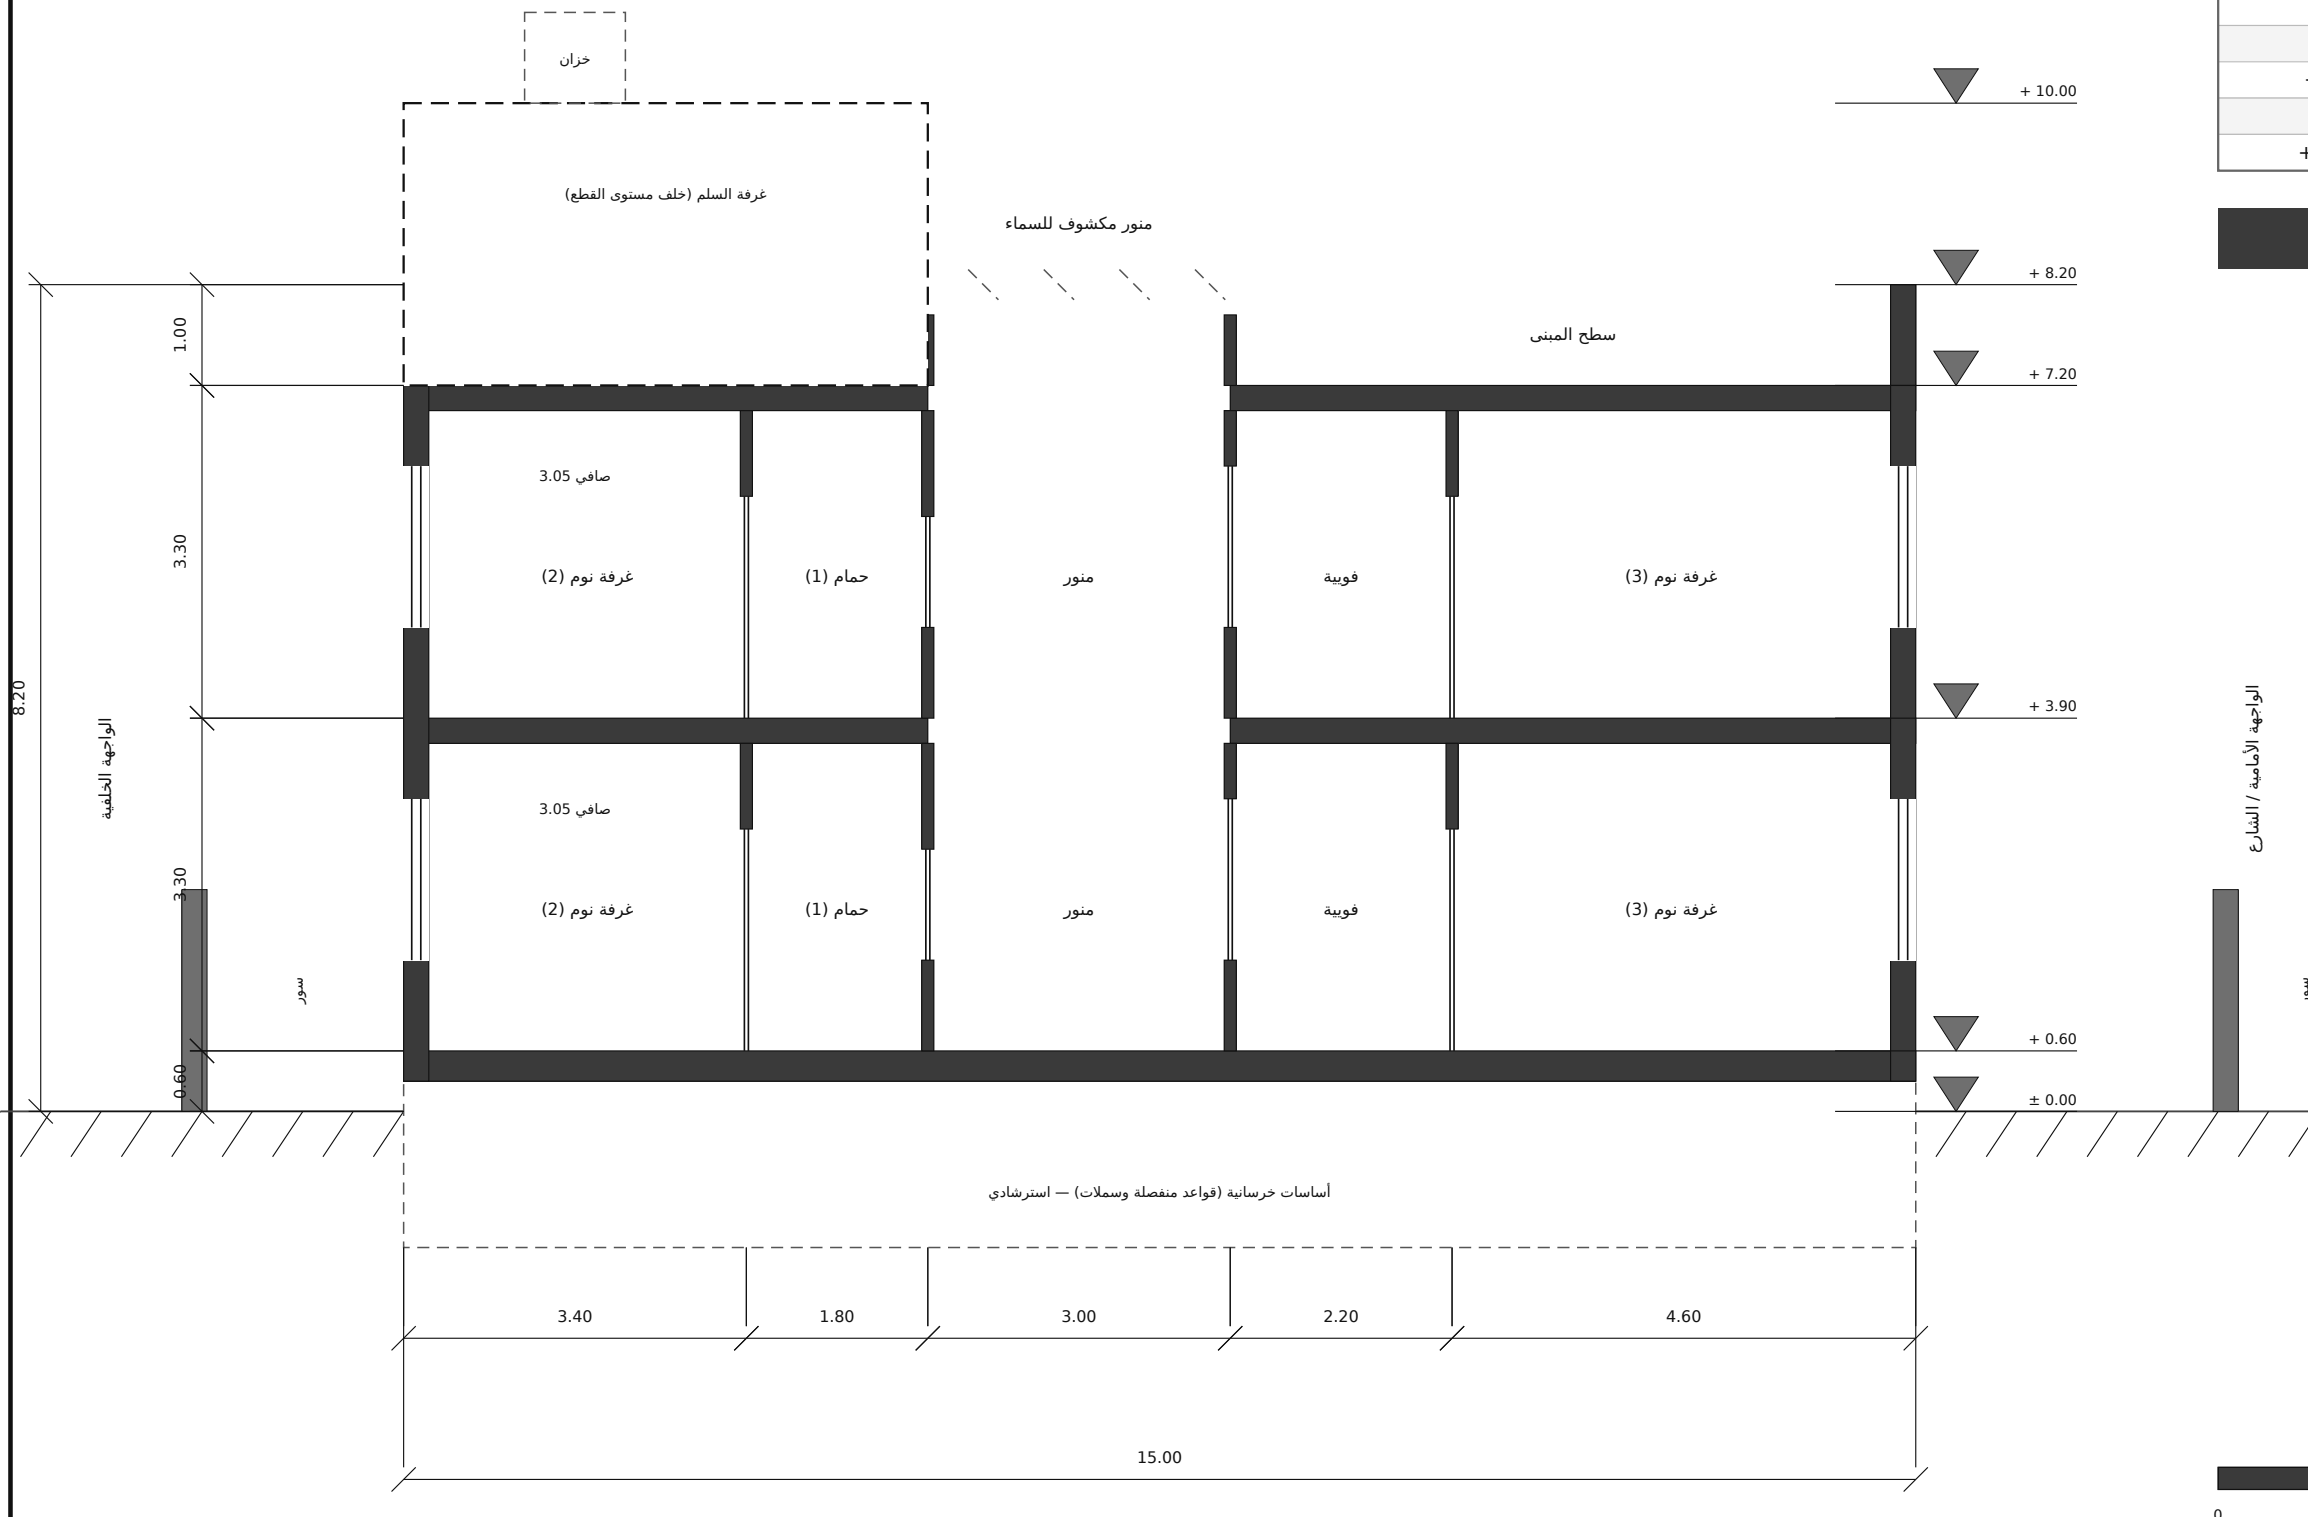منزل سكني بشقتين - قطعة أرض 400 م²

قطاع رأسي أ-أ

لوحة 04

رسم ابتدائي (تصميمي)

مقياس 1:75

الواجهة الأمامية

Front Elevation — 1:75

الواجهة الأمامية (جهة الشارع)



النشاطيات الخارجية

الحوائط	بياض أسمنتي + دهان واجهات
السرسيب والحزام	حجر هاشمي هيصم
الشبابيك	ألوميتال / PVC + زجاج مزدوج
باب المدخل	مصراعان زجاج وخشب معالج
الشرفات	درايزين معدني + حجر
سور السطح	سور ميان 1.00 م بكرانيش

ملاحظات الواجهة

- الواجهة الأمامية شمالية شرقية التوجيه،
- وتحقق إضاءة جيدة للصالة وغرفة النوم (3).
- مظلة خرسانية فوق باب المدخل عرض 2.00 م.
- يُفصل كاسرات شمس أفقية 0.40 م أعلى الشبابيك.
- منسوب أرضية الدور الأرضي + 0.60 م فوق
- منسوب الرصيف لحماية المبنى من مياه الأمطار.

مقياس رسم بياني (بالمتر)

منزل سكني بشقتين - قطعة أرض 400 م²

الواجهة الأمامية (الرئيسية)

لوحة 05

رسم ابتدائي (تصميمي)


مقياس 1:75

مسقط السطح

Roof Plan — 1:100

أعمال السطح

- عزل مائي (ممبرين) فوق طبقة ميول خرسانة خفيفة.
- عزل حراري 5 سم فوم أسفل بلاط المشايات.
- ميول 1.5% نحو 4 مصارف مطر قطر 4 بوصة.
- سور مباني ارتفاع 1.00 م حول السطح وحول المنور.
- خزانان علويان سعة 1000 لتر لكل شقة.
- قواعد خرسانية للخزانات ووحدات التكييف.
- غرفة السلم مسقوفة وبها باب خروج للسطح.
- السطح حتى ارتفاع لشقة الدور الأول.

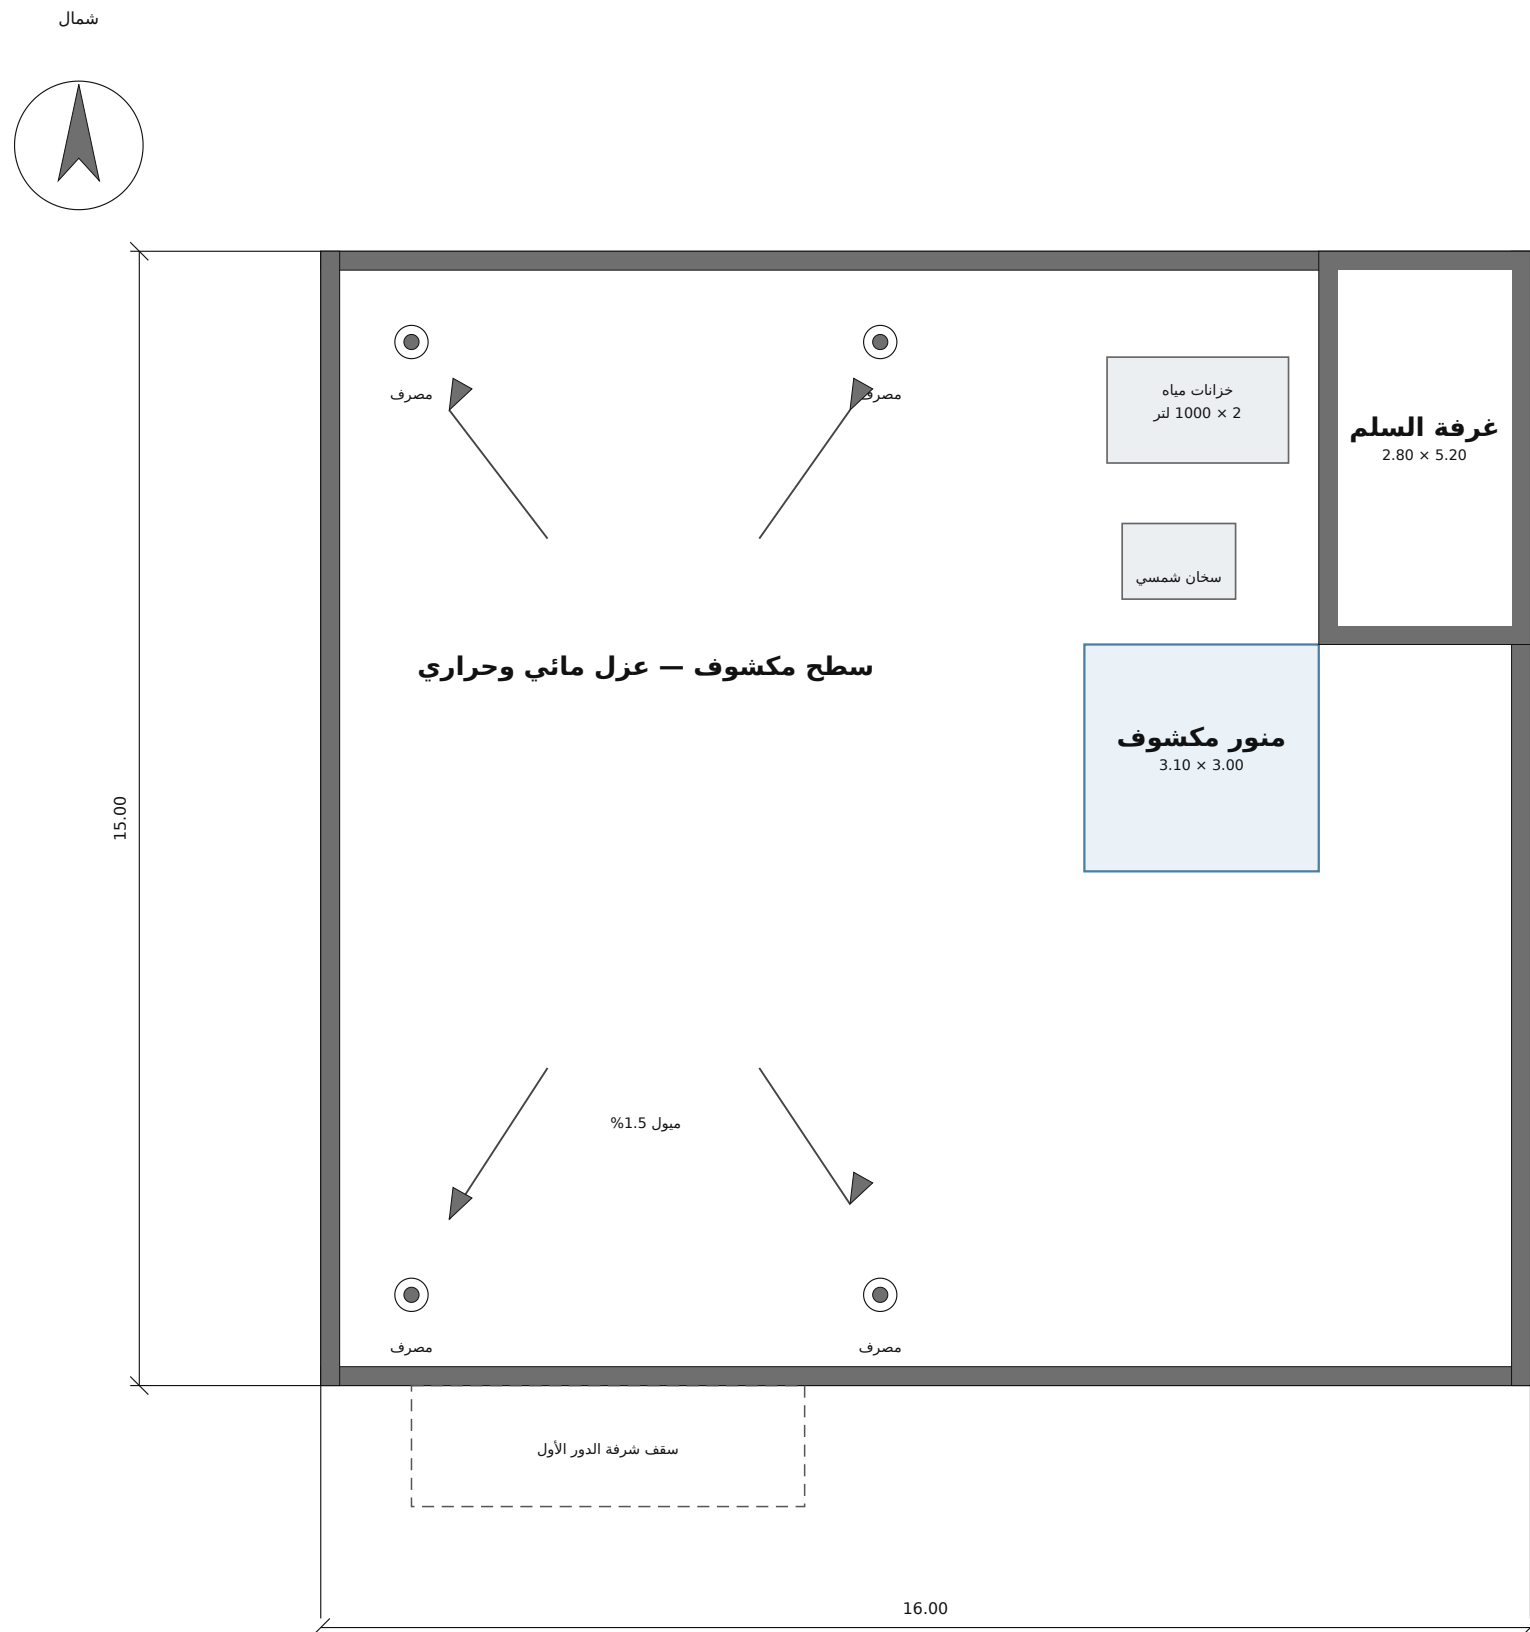

مقياس رسم بياني (بالمتر)



منزل سكني بشقتين - قطعة أرض 400 م²

مسقط السطح

لوحة 06

رسم ابتدائي (تصميمي)

مقياس 1:100